圖一　位置圖（廣域）

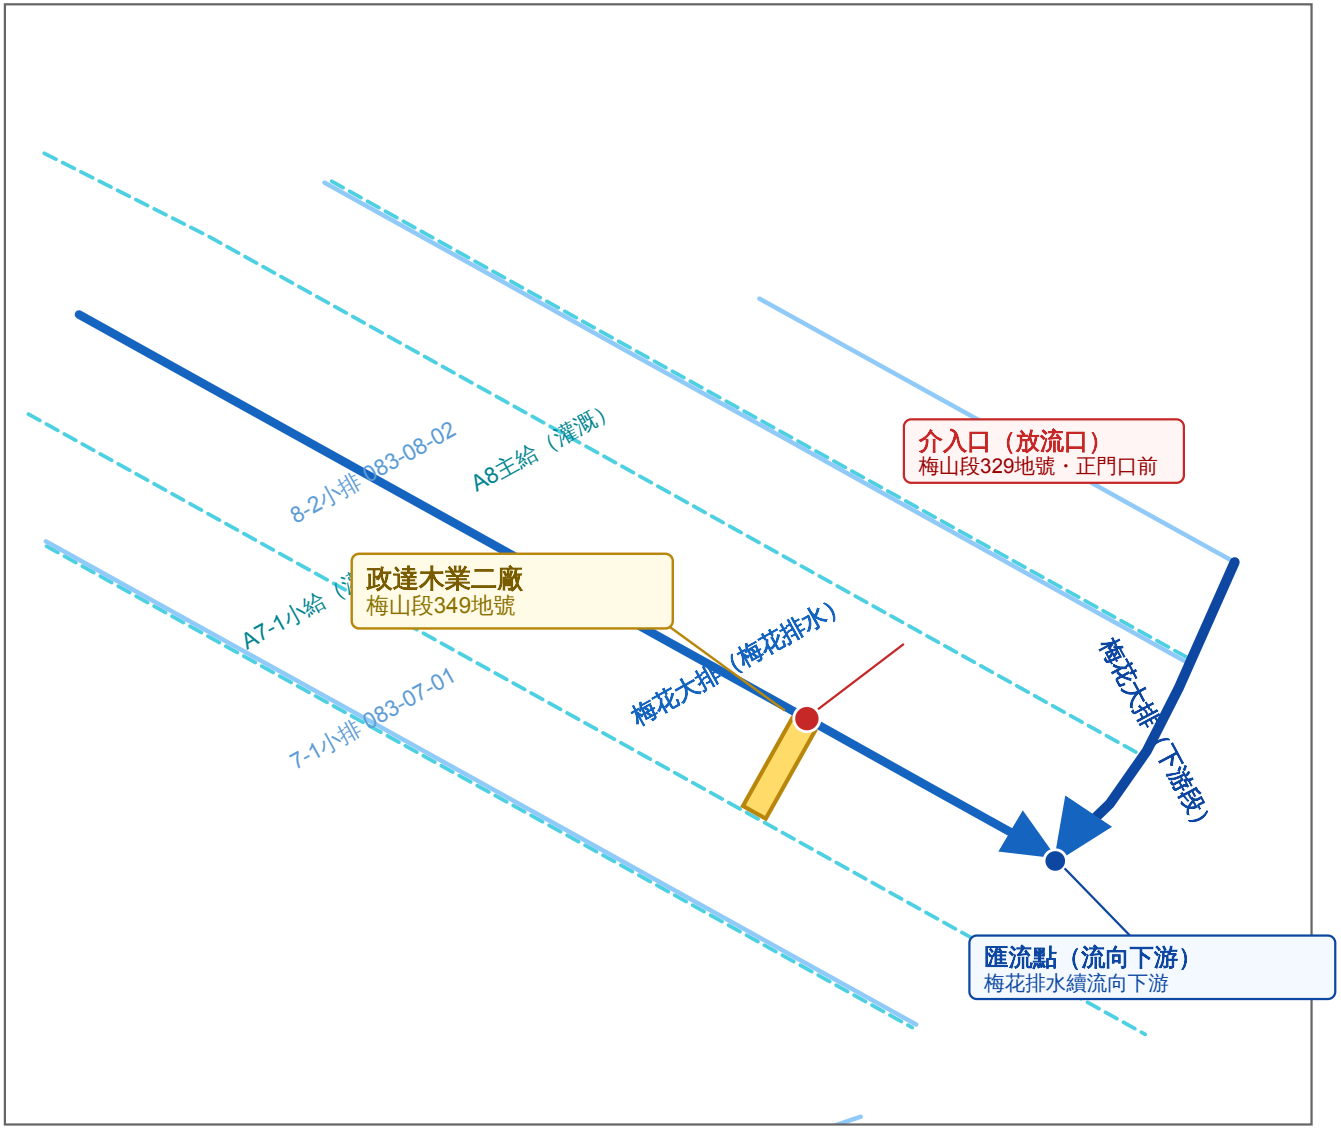


圖　例

- 政達木業二廠（梅山段349）
- 梅花大排（本次介入）
- 梅花大排下游段
- 其他排水渠道
- 灌溉渠道（不得排入）
- 介入口（放流口）
- 匯流點

放流口至承受水體流路

- ● 廠內化糞池／放流池（梅山段349）
- ▼ 介入口（梅山段329　水利用地）
- ▼ 梅花排水（梅山段329地號）
- ▼ 流向東南下游
- ▼ （宜蘭縣政府轄管區域排水）
- ▼ 梅花排水（圖外下游）

重要提醒

廠區西南側 4.1 公尺處為 A7-1小給，性質為「灌溉渠道」。依農田水利法第14條第1項，灌溉專用渠道原則禁止排放非農田排水，本案放流口不得設於該渠道，須由東北側接入梅花排水。

比例尺　約 1：7019（A4 橫向）

0　100　200　300　400　公尺

N


底圖來源：農業部農田水利署宜蘭管理處「農田水利渠道查詢系統」渠道圖層（Canal民眾查詢1140917）
查詢日期 115.08.28　座標系統 TWD97 二度分帶（EPSG:3826）
註：渠道線形為圖資，僅供位置參考；實際位置及流向依現地與管理處初勘為準。

圖一　位置圖（廣域）

廠區位置與排水系統，放流口至承受水體

案名：政達木業有限公司二廠生活污水搭排
｜　TWD97 二度分帶　｜　第 1 張，共 6 張

圖二　介入點位置圖（平面圖）

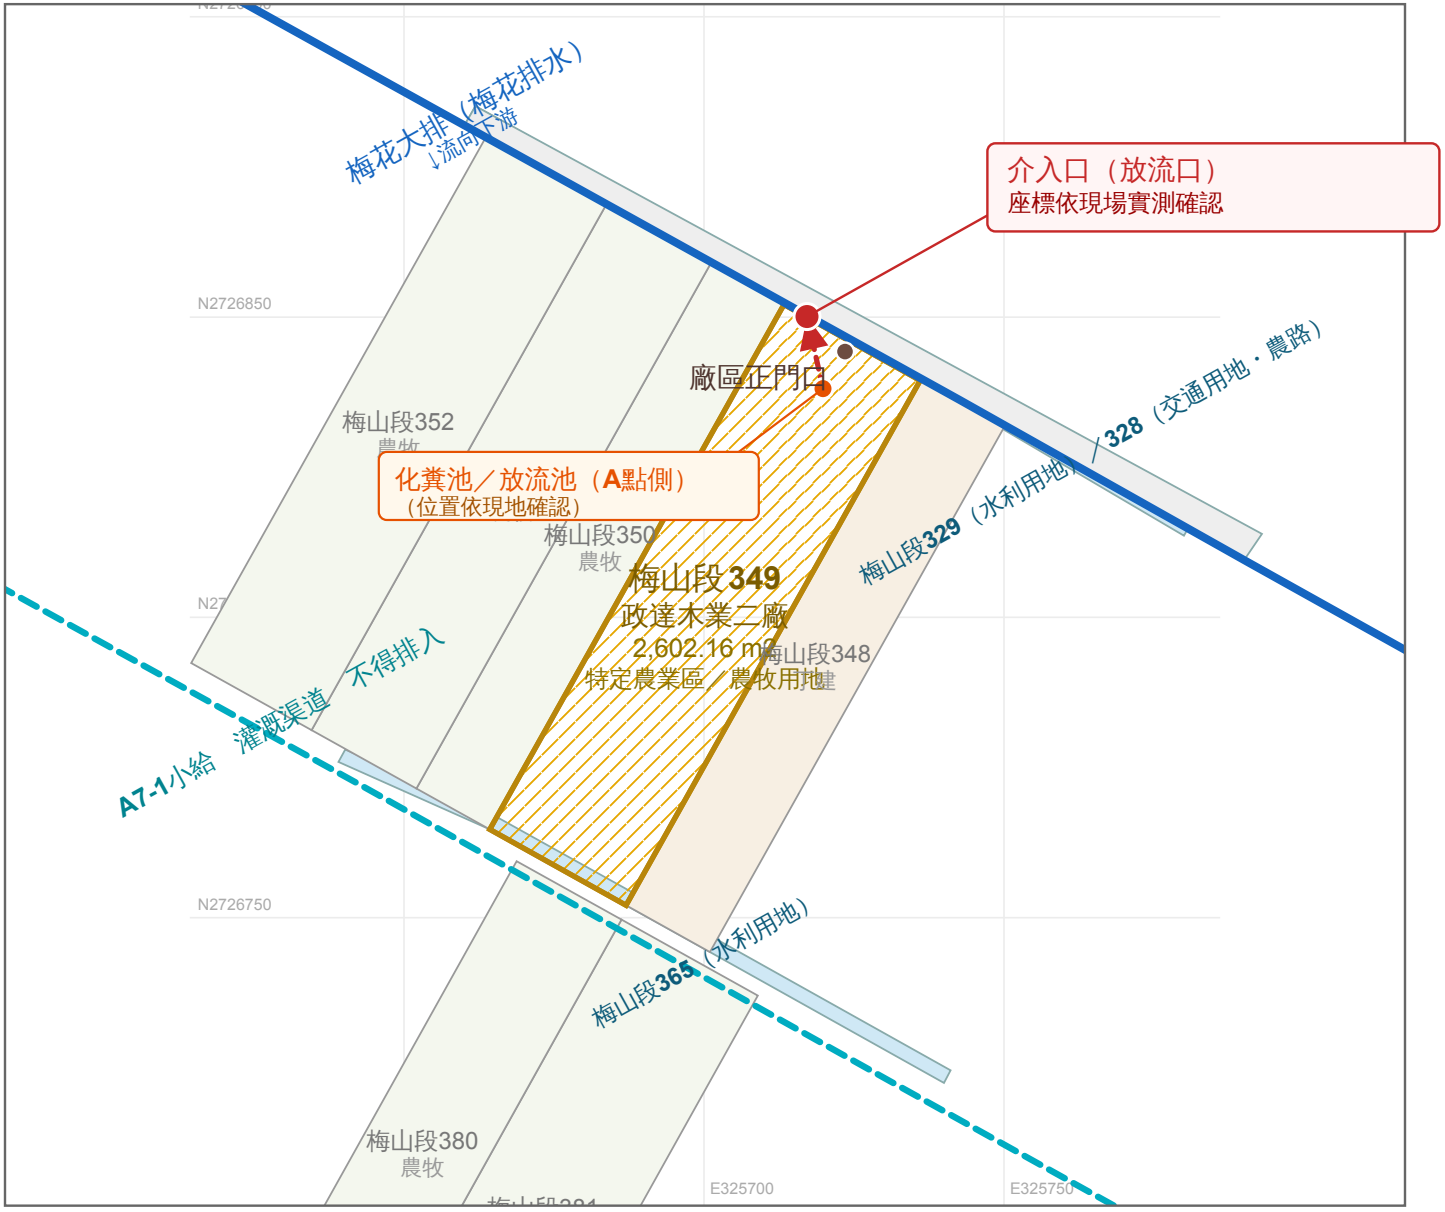

比例尺　約**1**：**1260**（**A4** 向）

0　20　40　60　80　公尺

N

底圖來源：農業部農田水利署宜蘭管理處「農田水利渠道查詢系統」
地籍圖層114Oct地籍圖／渠道圖層Canal民眾查詢1140917　查詢日期115.08.28
註：渠道中心線為圖資線形，與現地略有偏差；介入口位置、椿號、坐標及渠道斷面依初勘實測為準。

圖　例

- 申請搭排土地（梅山段349）
- 水利用地（329／365）
- 交通用地（328　農路）
- 農牧用地
- 丁種建築用地
- 排水渠道　梅花大排（可搭排）
- 灌溉渠道　A7-1小給（禁止排入）
- 擬設放流管線
- 介入口（放流口）
- 化糞池／放流池

介入渠道：梅花排水（梅花大排）

放流口至承受水體流路

- ●廠內化糞池／放流池
- ▼介入口（梅山段329地號）
- ▼梅花排水（本次介入承受水體）
- ▼流向下游（宜蘭縣政府轄管區域排水）
- ▼梅花排水（承受水體）

案件資


申請人	政達木業有限公司二廠
負責人	陳文政
廠　址	冬山鄉得安村梅林路571-1號
納管編號	P0200190
排放水量	日最大2.25 m³／年最大821.25 m³

圖二　介入點位置圖（平面圖）

含放流口位置至承受水體

案名：政達木業有限公司二廠生活污水搭排
｜　TWD97 二度分帶　｜　第2張，共6張

圖三　地籍圖套繪圖

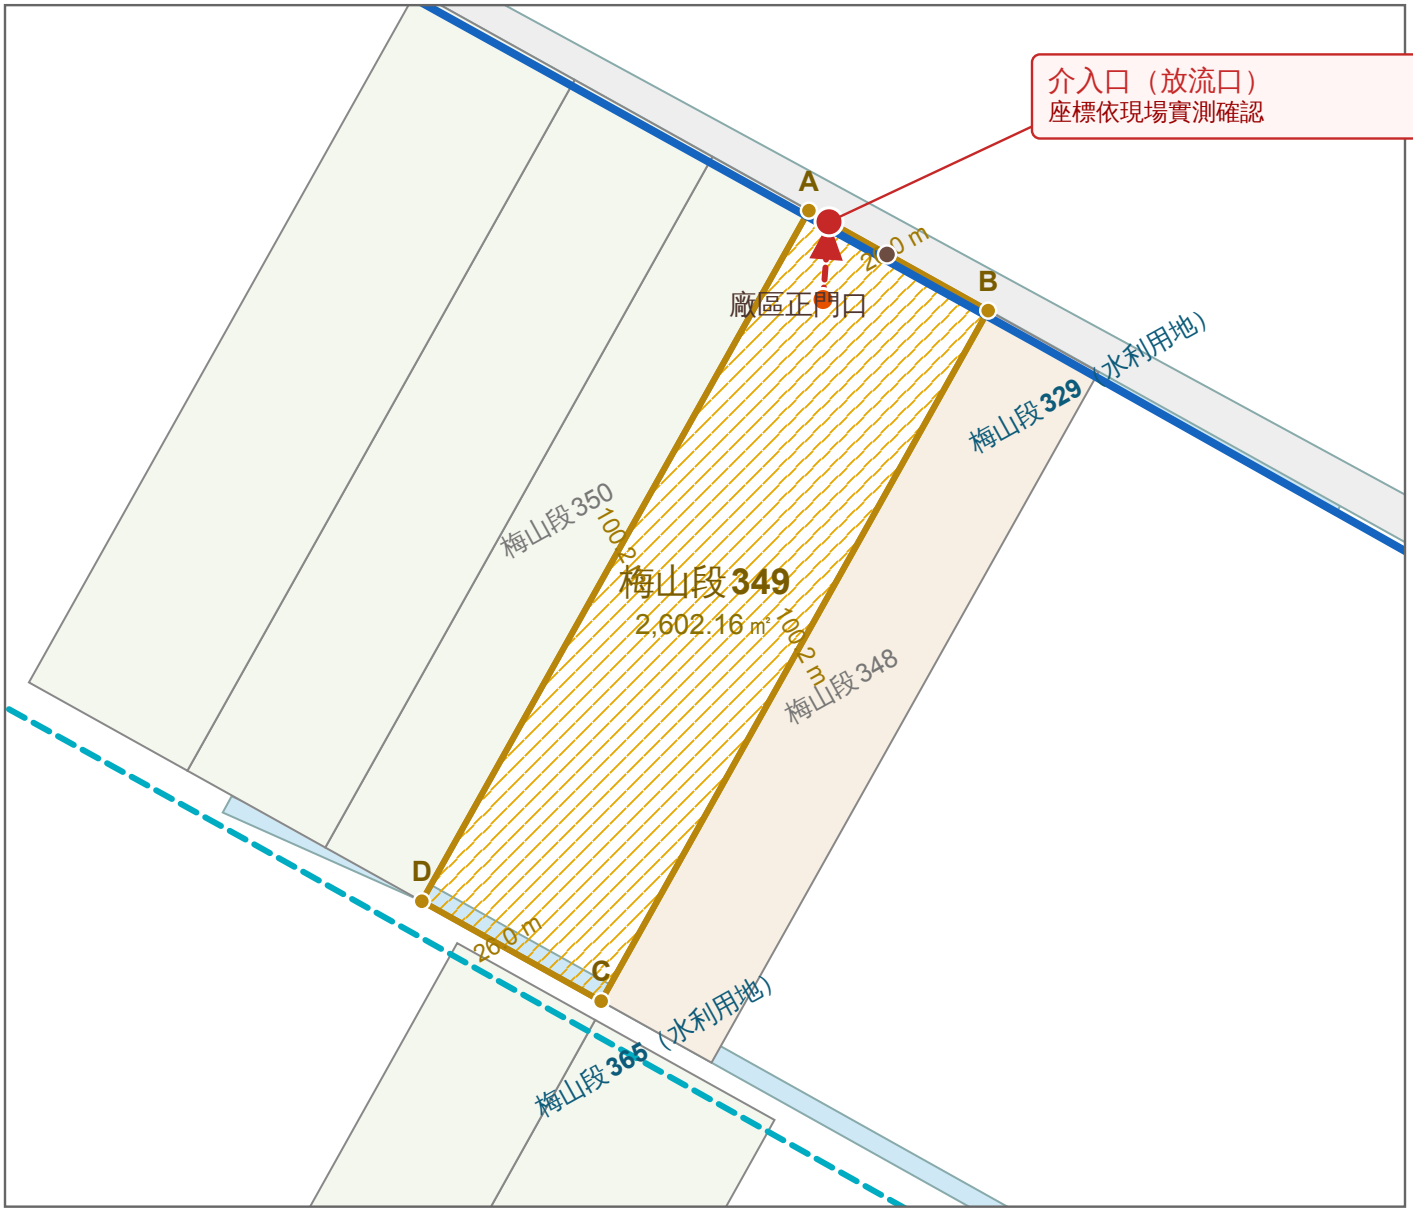

界址點坐標（TWD97 二度分帶）

點號	E（m）	N（m）
A	325713.33	2726852.09
B	325736.04	2726839.44
C	325687.01	2726752.07
D	325664.29	2726764.71

介入口　依現場實測　　確認

坐標為圖資推估值，界址以複丈鑑界結果為準。
介入口位置依管理處初勘確認。

土地標示

地　號	宜蘭縣冬山鄉梅山段349地號
重測前	梅花段1708-0000
面　積	2,602.16平方公尺
使用分區	特定農業區
用地類別	農牧用地
所有權人	陳文政（全部1分之1）
謄本字號	羅東謄字第014081號
核發日期	民國115年8月28日

地號

東北：梅山段329（水利用地）←介入口
西南：梅山段365（水利用地）
東南：梅山段348（丁種建築用地）
西北：梅山段350（農牧用地）

比例尺　約**1**：**958**（**A4** 向）

0　10　20　30　40　公尺

N


底圖來源：農業部農田水利署宜蘭管理處渠道查詢系統地籍圖層（114Oct地籍圖）；地籍圖謄本：宜蘭縣羅東地政事務所羅東謄字第014081號（115.08.28，1/500）。
註：本圖為套繪示意，界址以複丈鑑界結果為準；正式送件請於地籍圖謄本正本上套繪搭排位置並簽章。

圖三　地籍圖套繪圖

搭排位置套繪於地籍圖

案名：政達木業有限公司二廠生活污水搭排
｜　TWD97 二度分帶　｜　第3張，共6張

圖四　借用他人土地　管線位置圖說

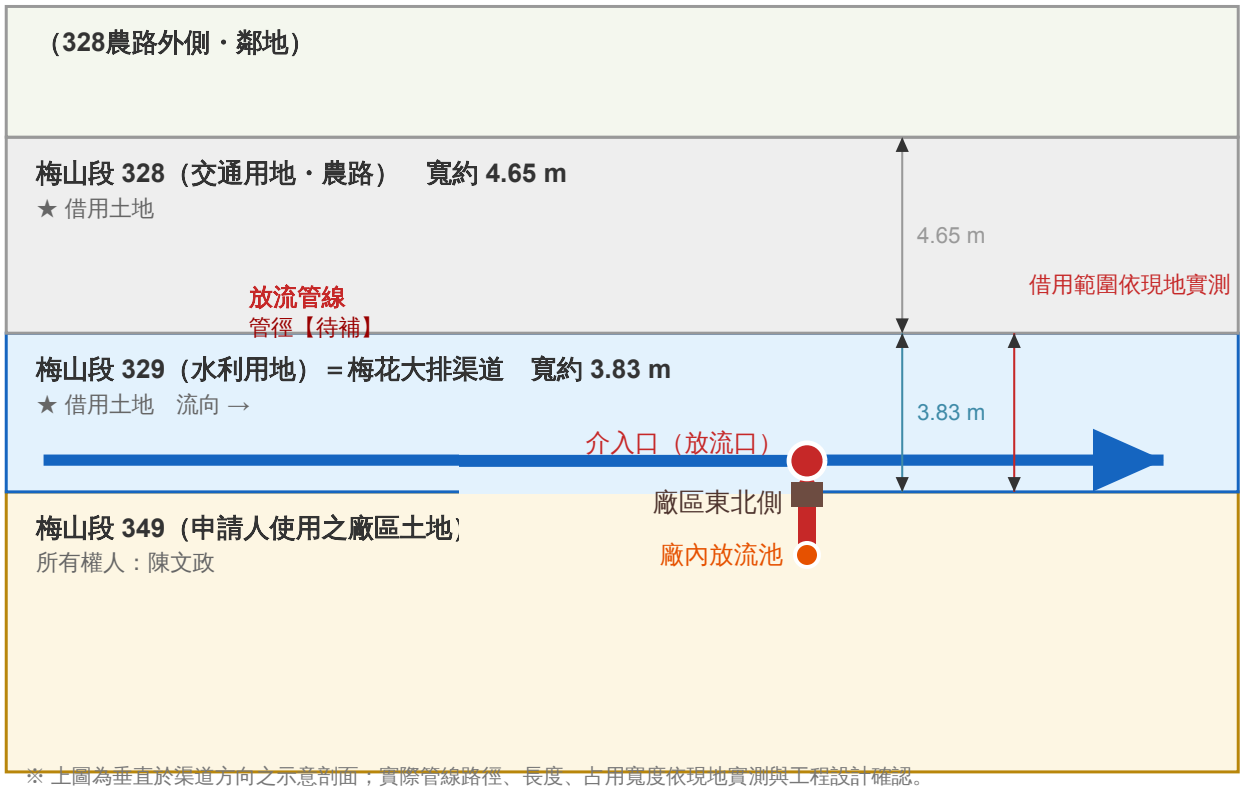

※ 上圖為垂直於渠道方向之示意剖面；實際管線路徑、長度、占用寬度依現地實測與工程設計確認。

鄰接公有土地明細

地號	用地類別	通過長度	面積
梅山段329	水利用地	約 3.83 m	2,090.9㎡
梅山段328	交通用地	—	5,123.8㎡

占用寬度：以管徑計（【待補】）
埋設深度：【待補】 m
施設方式：☐ 埋管　☐ 附掛　☐ 明溝銜接
兩筆土地均為公有性質用地。依官方應檢附文件三，需使用之土地如已依農田水利法第23條第1項納入農田水利事業作業基金者，得免附土地使用同意證明；權屬請調謄本並洽羅東工作站確認。

施設承諾

1. 管線施設不妨礙農路通行及渠道通水。
2. 施工前 7 日通知管理處及羅東工作站，會同放樣後始得施工。
3. 路面及護岸開挖後即時復舊，回復原狀。
4. 損壞農田水利設施或農路者，由本公司負責無條件修復或賠償。
5. 許可期間屆滿或廢止時，自費拆除管線並回復原狀。

介入口坐標（TWD97）


E　325727.90
N　2726851.58
椿號：依初勘實測為準

圖四　借用他人土地管線位置圖說
管線通過梅山段329地號（梅花大排渠道）

案名：政達木業有限公司二廠生活污水搭排
示意圖（尺寸待實測）　|　TWD97 二度分帶　|　第 4 張，

註：本圖為官方應檢附文件「借用他人土地者，應含設置於其土地管線位置圖說」之圖說。實際借用範圍、長度及是否須另取得土地使用同意，依地籍謄本權屬及管理處初審結果為準。

圖五　排水系統流路圖

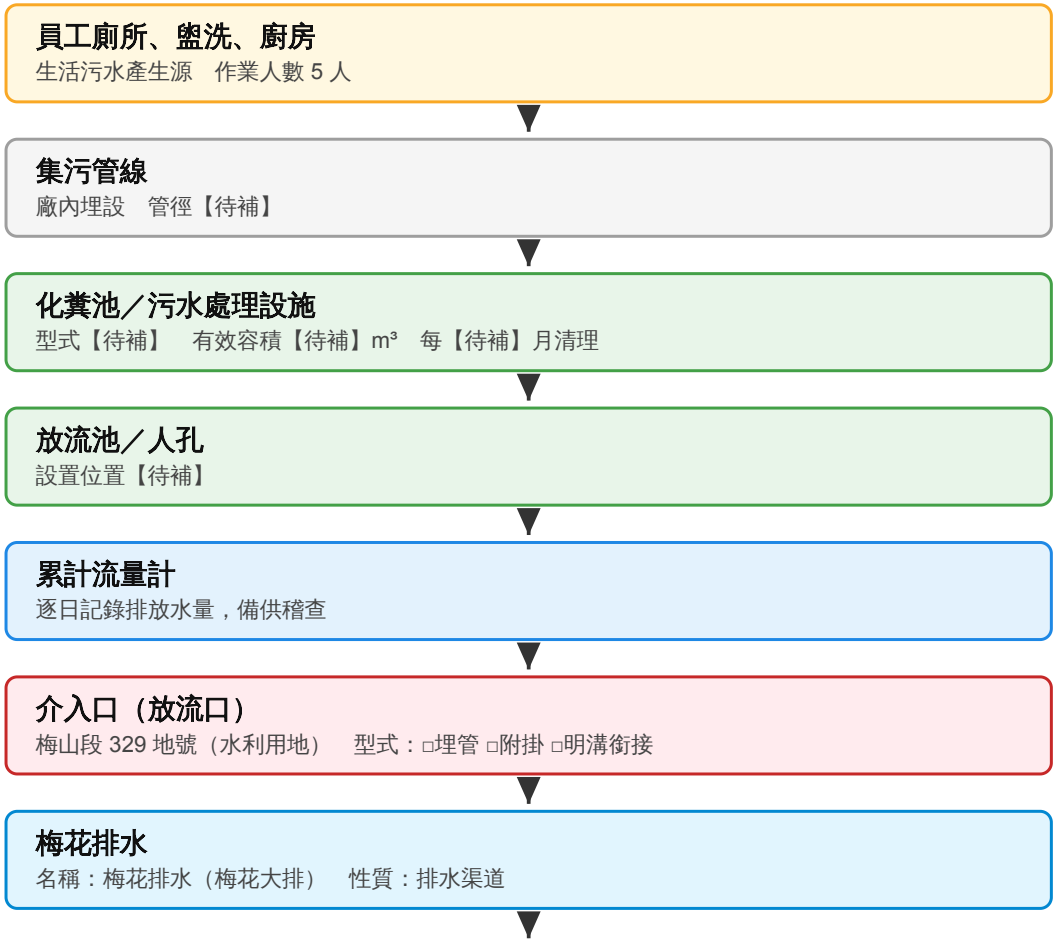

排放水量

作業人數	5 人
單位污水量	150 公升／人·日
日平均排放量	0.75 m³
尖峰係數	3.0
日最大排放量	2.25 m³
年搭排日數	365日
年最大排放量	821.25 m³

計算依據

內政部「建築物污水處理設施設計技術規範」
表2-1　C-1 工廠（廠房）類
單位污水量 150 公升／人·日
（規範得按作業人數1/4計，本案不折減，
以全員5人計算，屬保守估計）

排放水性質

僅生活污水（廁所、盥洗、廚房）
無製程廢水：木材裁切、刨光、砂磨、
組裝、乾燥等乾式加工，製程不產生廢水
納管申請書已聲明：屬低污染行業別，
製程不含脫脂、酸洗、電鍍或陽極處理
（納管編號 P0200190）


註：【待補】[illegible]

圖五　排水系統流路圖
生活污水自產生源至承受水體

案名：政達木業有限公司二廠生活污水搭排
示意圖（無比例）　|　TWD97 二度分帶　|　第 5 張，共 6


圖六　介入口工程設計圖（平面・剖面）

（一）平面圖

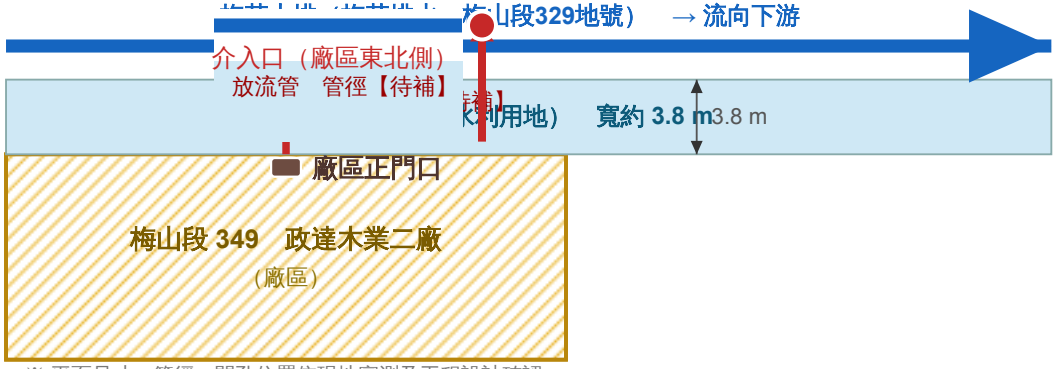

※ 平面尺寸、管徑、開孔位置依現地實測及工程設計確認

（二）縱剖面圖

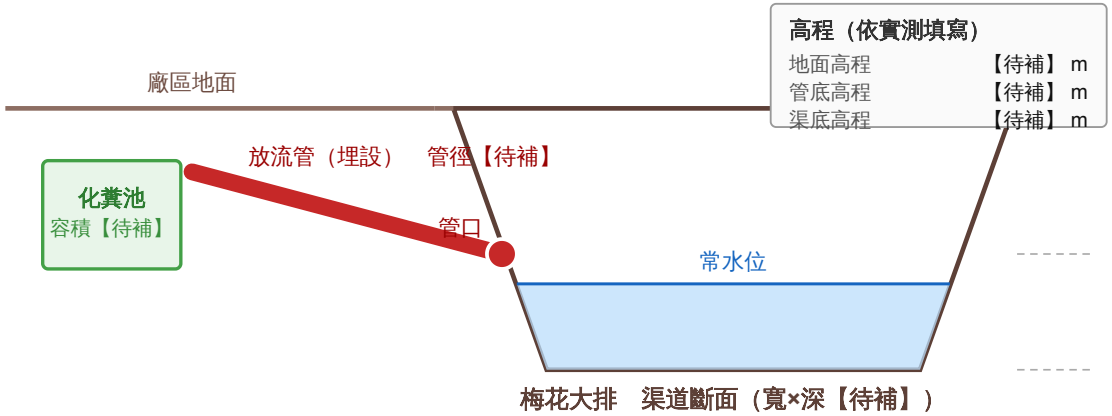

※ 高程、管徑、渠道斷面尺寸依現地實測填寫；施工前7日通知管理處及工作站會同放樣。

介入口規格（待填）

介入口型式	□ 埋管　□ 附掛　□ 明溝銜接
管材	【待補】
管徑	【待補】 mm
管底高程	【待補】 m
渠道底高程	【待補】 m
渠道斷面（寬×深）	【待補】
護岸開孔尺寸	【待補】
回填與復舊方式	【待補】
施工廠商	【待補】

施工承諾事項

1. 施工前 7 日通知管理處及羅東工作站，會同放樣後始得施工。
2. 施工期間不阻斷渠道通水，必要時設置臨時導水設施。
3. 施工損壞農田水利設施者，由本公司負責無條件修復或賠償。
4. 竣工後 30 日內報請管理處查驗。
5. 避開灌溉期施工；如須於灌溉期施工，事先報經管理處同意。
6. 工程費用由本公司負擔。

圖六　介入口工程設計圖

平面圖・縱剖面圖

案名：政達木業有限公司二廠生活污水搭排
示意圖（尺寸待實測）　|　TWD97 二度分帶　|　第 6 張，