# 圖一　位置圖（廣域）

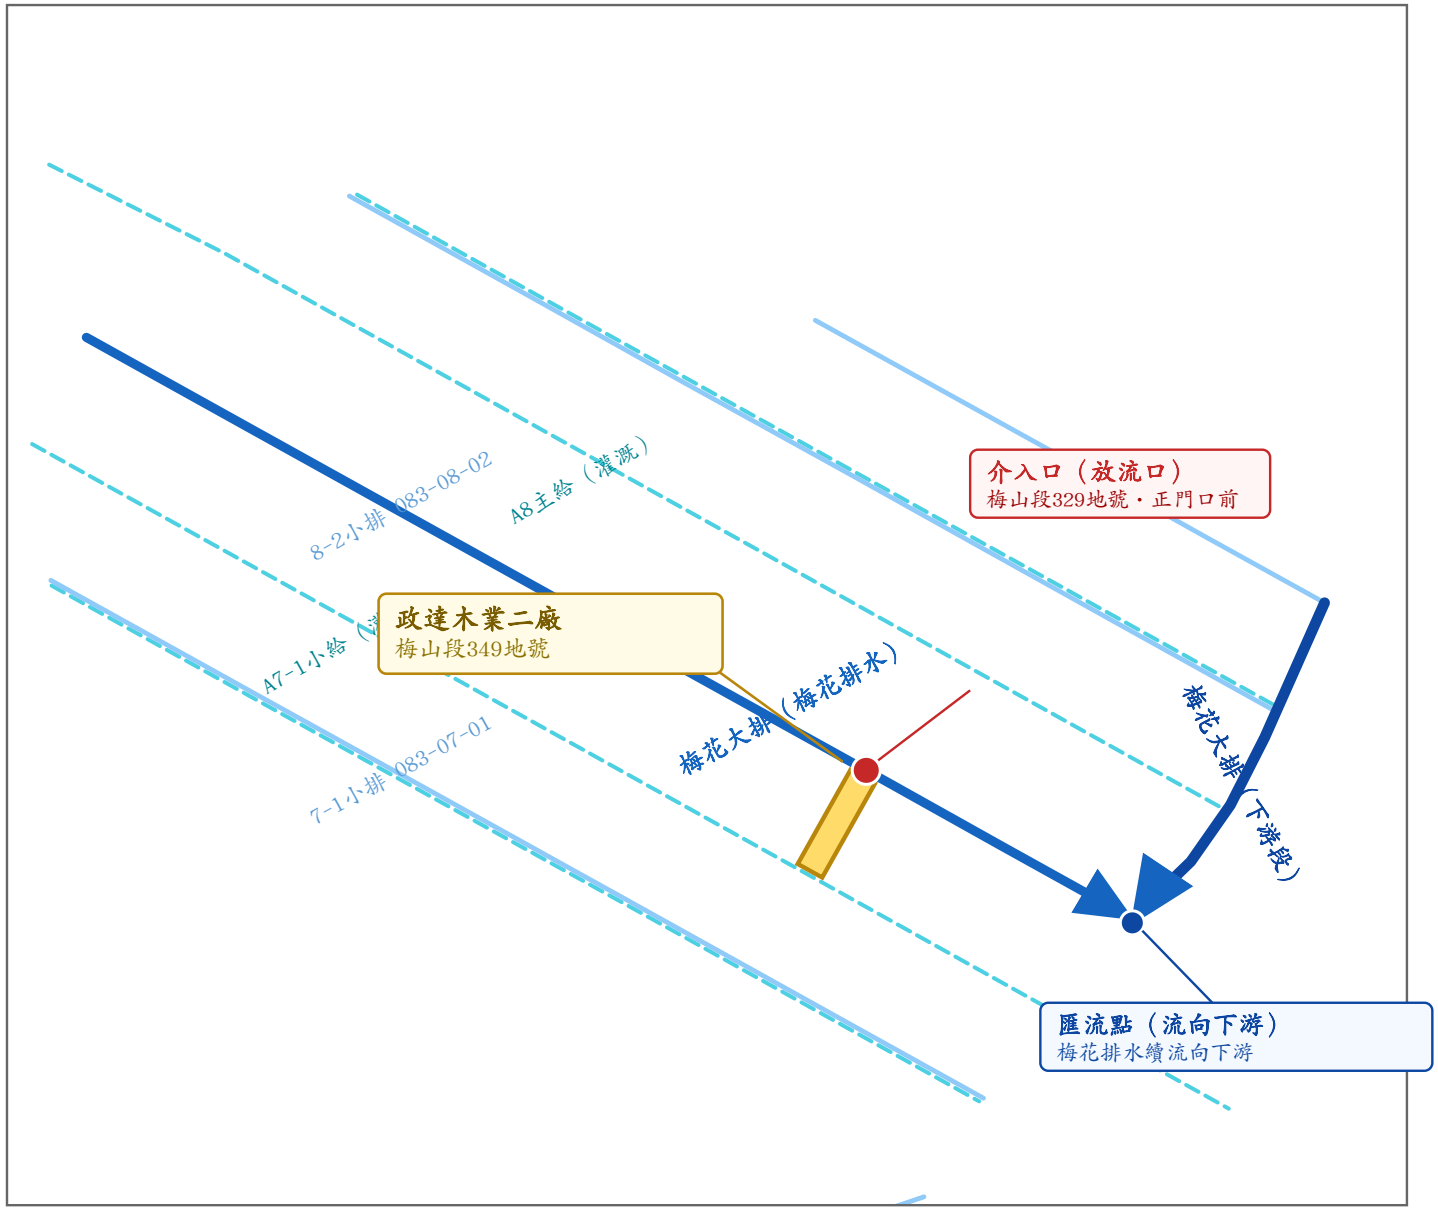



**圖　例**

- 政達木業二廠（梅山段349）
- 梅花大排（本次介入）
- 梅花大排下游段
- 其他排水渠道
- 灌溉渠道（不得排入）
- 介入口（放流口）
- 匯流點

**放流口至承受水體流路**

- ● 廠內化糞池／放流池（梅山段349）
- ▼ 介入口（梅山段329　水利用地）
- ▼ 梅花排水（梅山段329地號）
- ▼ 流向東南下游
- ▼ （宜蘭縣政府轄管區域排水）
- ▼ 梅花排水（圖外下游）

**重要提醒**

廠區西南側 4.1 公尺處爲 A7-1小給，性質爲「灌溉渠道」。依農田水利法第14條第1項，灌溉專用渠道原則禁止排放非農田排水，本案放流口不得設於該渠道，須由東北側接入梅花排水。

比例尺　約 1：7019（A4 橫向）

0　100　200　300　400　公尺

N


底圖來源：農業部農田水利署宜蘭管理處「農田水利渠道查詢系統」渠道圖層（Cana1民眾查詢1140917）
查詢日期 115.08.28　座標系統 TWD97 二度分帶（EPSG:3826）
註：渠道線形爲圖資，僅供位置參考；實際位置及流向依現地與管理處初勘爲準。

**圖一　位置圖（廣域）**

廠區位置與排水系統，放流口至承受水體

案名：政達木業有限公司二廠生活污水搭排
｜ TWD97 二度分帶 ｜ 第 1 張，共 6 張

# 圖二　介入點位置圖（平面圖）

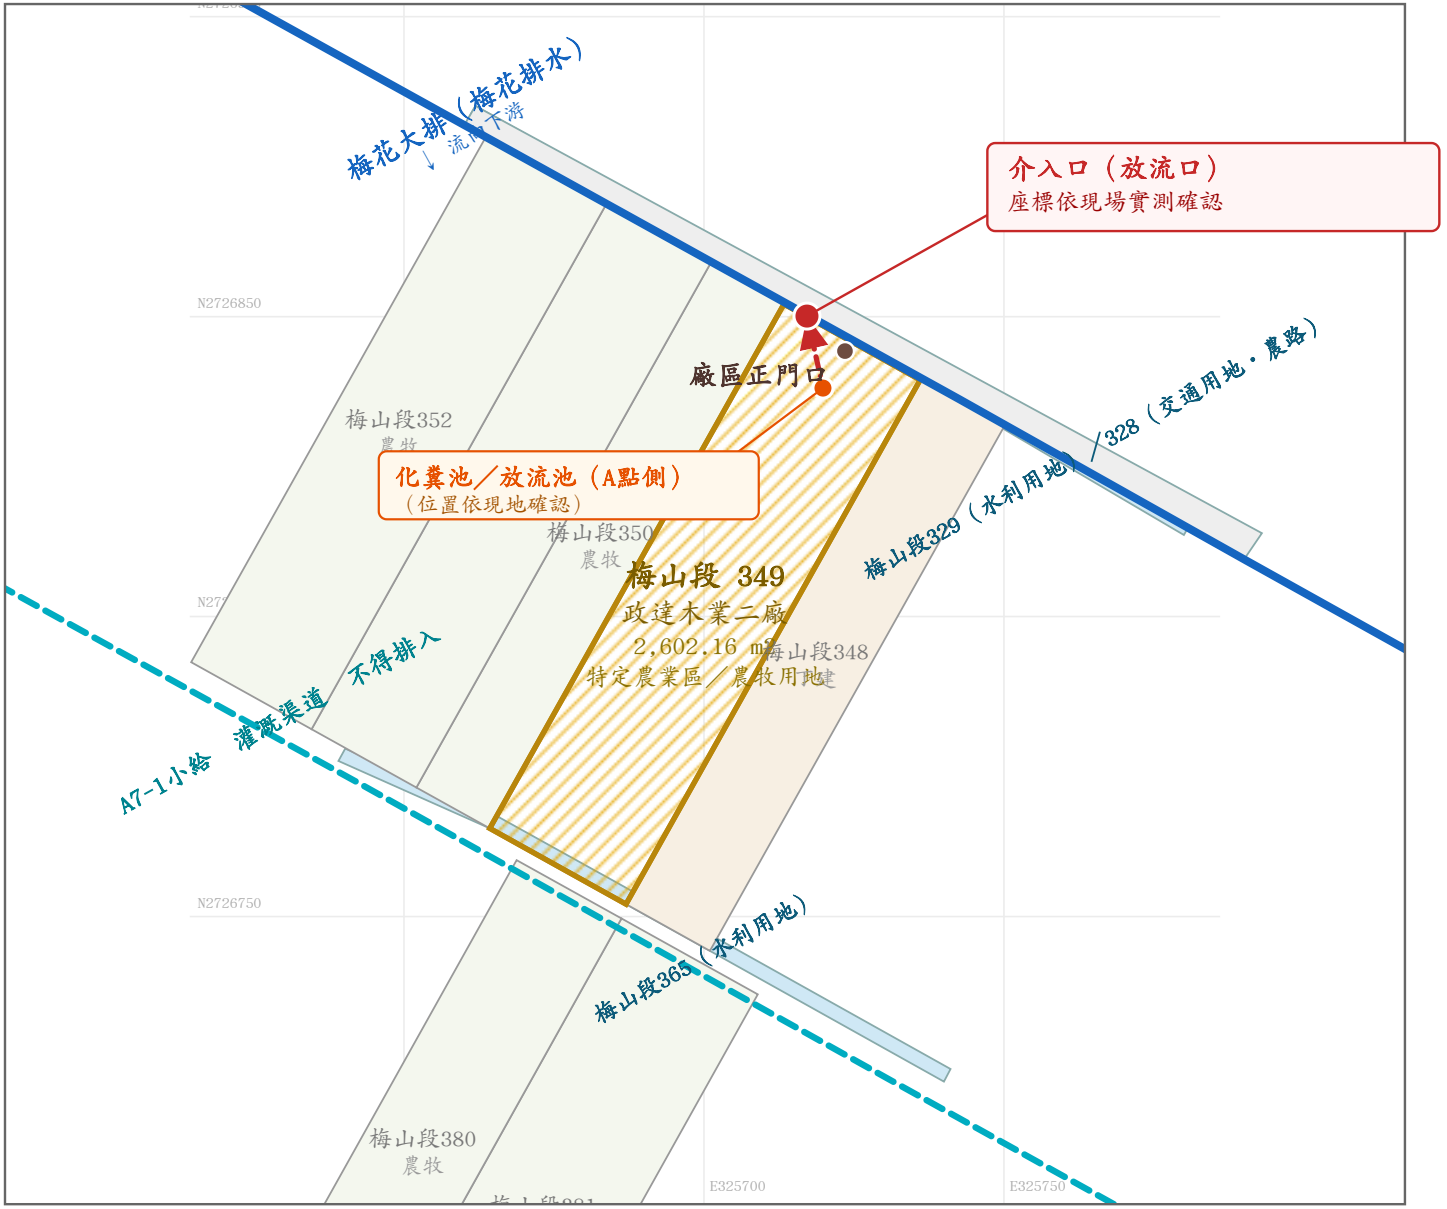


## 圖　例

- 申請搭排土地（梅山段349）
- 水利用地（329／365）
- 交通用地（328　農路）
- 農牧用地
- 丁種建築用地
- 排水渠道　梅花大排（可搭排）
- 灌溉渠道　A7-1小給（禁止排入）
- 擬設放流管線
- 介入口（放流口）
- 化糞池／放流池

介入渠道：梅花排水（梅花大排）

## 放流口至承受水體流路

- ● 廠內化糞池／放流池
- ▼ 介入口（梅山段329地號）
- ▼ 梅花排水（本次介入承受水體）
- ▼ 流向下游（宜蘭縣政府轄管區域排水）
- ▼ 梅花排水（承受水體）

## 案件資料

| | |
|---|---|
| 申請人 | 政達木業有限公司二廠 |
| 負責人 | 陳文政 |
| 廠　址 | 冬山鄉得安村梅林路571-1號 |
| 納管編號 | P0200190 |
| 排放水量 | 日最大 2.25 ㎥／年最大 821.25 ㎥ |

比例尺　約 1：1260（A4 橫向）

0　20　40　60　80　公尺

N


底圖來源：農業部農田水利署宜蘭管理處「農田水利渠道查詢系統」
地籍圖層 1140ct地籍圖／渠道圖層 Cana1民眾查詢1140917　查詢日期 115.08.28
註：渠道中心線爲圖資線形，與現地略有偏差；介入口位置、椿號、坐標及渠道斷面依初勘實測爲準。

**圖二　介入點位置圖（平面圖）**

含放流口位置至承受水體

案名：政達木業有限公司二廠生活污水搭排

# 圖三　地籍圖套繪圖

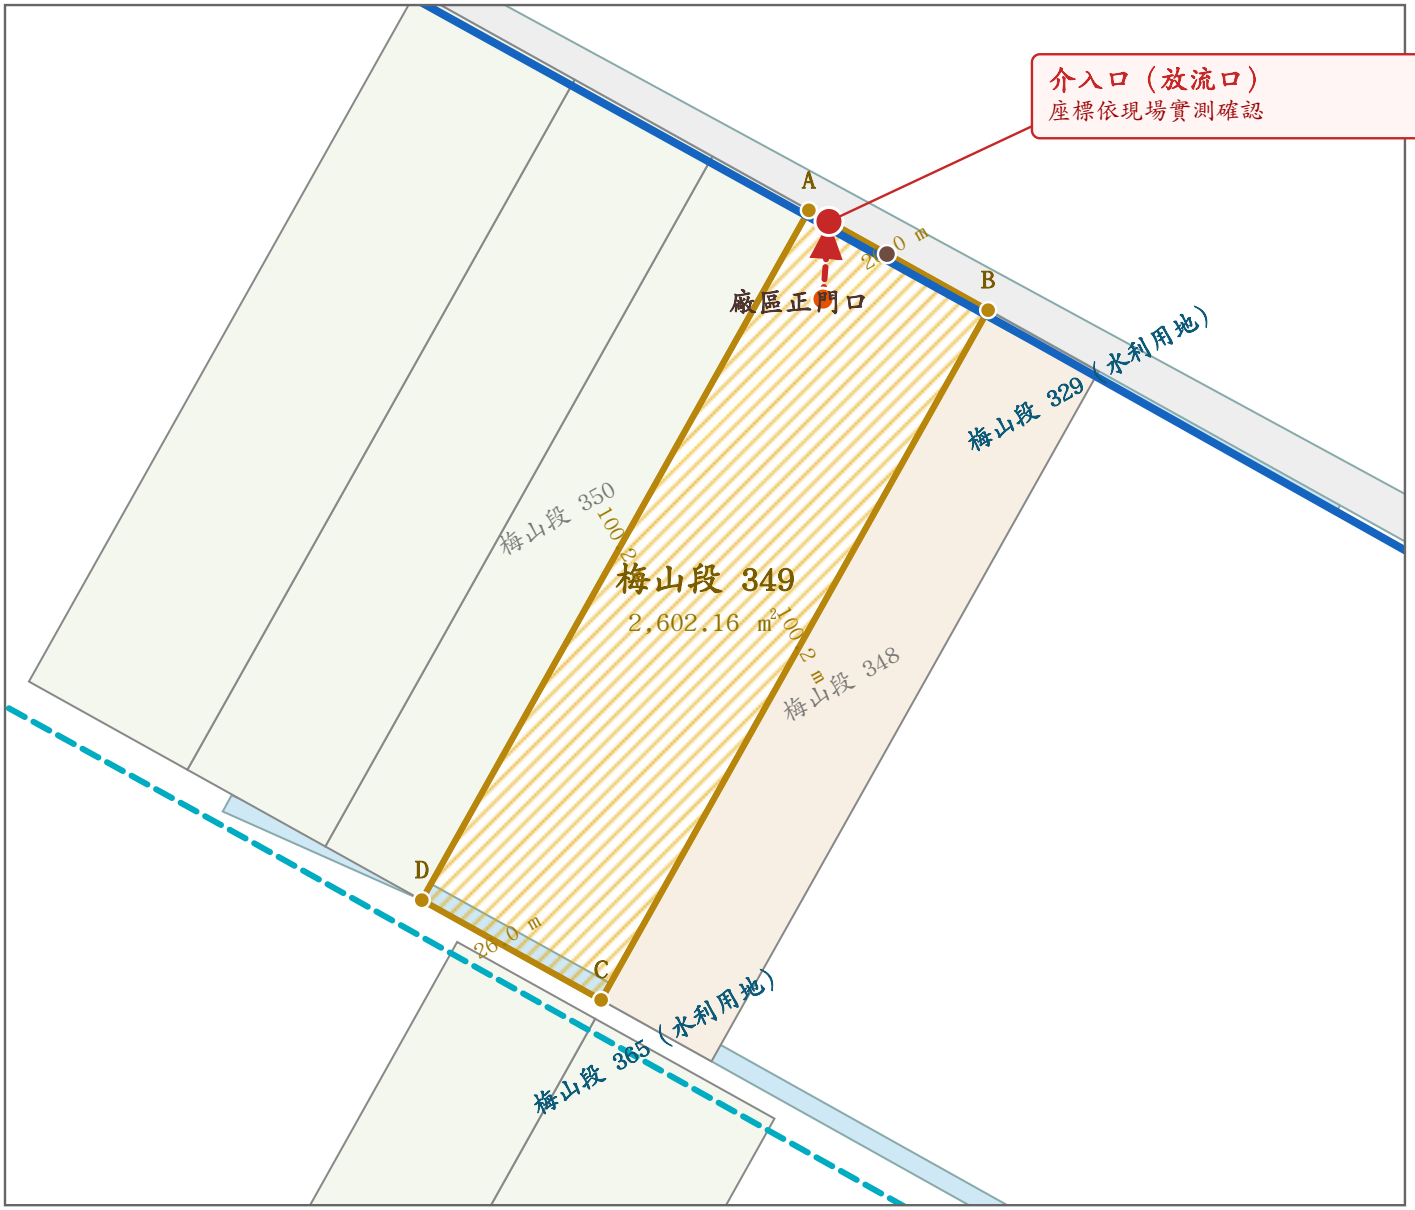


## 界址點坐標（TWD97 二度分帶）

| 點號 | E（m） | N（m） |
|---|---|---|
| A | 325713.33 | 2726852.09 |
| B | 325736.04 | 2726839.44 |
| C | 325687.01 | 2726752.07 |
| D | 325664.29 | 2726764.71 |

介入口　依現場實測　確認

坐標爲圖資推估值，界址以複丈鑑界結果爲準。
介入口位置依管理處初勘確認。

## 土地標示

| | |
|---|---|
| 地　號 | 宜蘭縣冬山鄉梅山段349地號 |
| 重測前 | 梅花段 1708-0000 |
| 面　積 | 2,602.16 平方公尺 |
| 使用分區 | 特定農業區 |
| 用地類別 | 農牧用地 |
| 所有權人 | 陳文政（全部 1分之1） |
| 謄本字號 | 羅東謄字第014081號 |
| 核發日期 | 民國115年8月28日 |

## 相鄰地號

東北：梅山段329（水利用地）← 介入口
西南：梅山段365（水利用地）
東南：梅山段348（丁種建築用地）
西北：梅山段350（農牧用地）

比例尺　約 1：958（A4 橫向）

0　10　20　30　40　公尺

N

底圖來源：農業部農田水利署宜蘭管理處渠道查詢系統地籍圖層（1140ct地籍圖）；地籍圖謄本：宜蘭縣羅東地政事務所 羅東謄字第014081號（115.08.28，1/500）


註：本圖爲套繪示意，界址以複丈鑑界結果爲準；正式送件請於地籍圖謄本正本上套繪搭排位置並簽章。

## 圖三　地籍圖套繪圖

搭排位置套繪於地籍圖

案名：政達木業有限公司二廠生活污水搭排
｜ TWD97 二度分帶 ｜ 第 3 張，共 6 張

# 圖四　借用他人土地　管線位置圖說

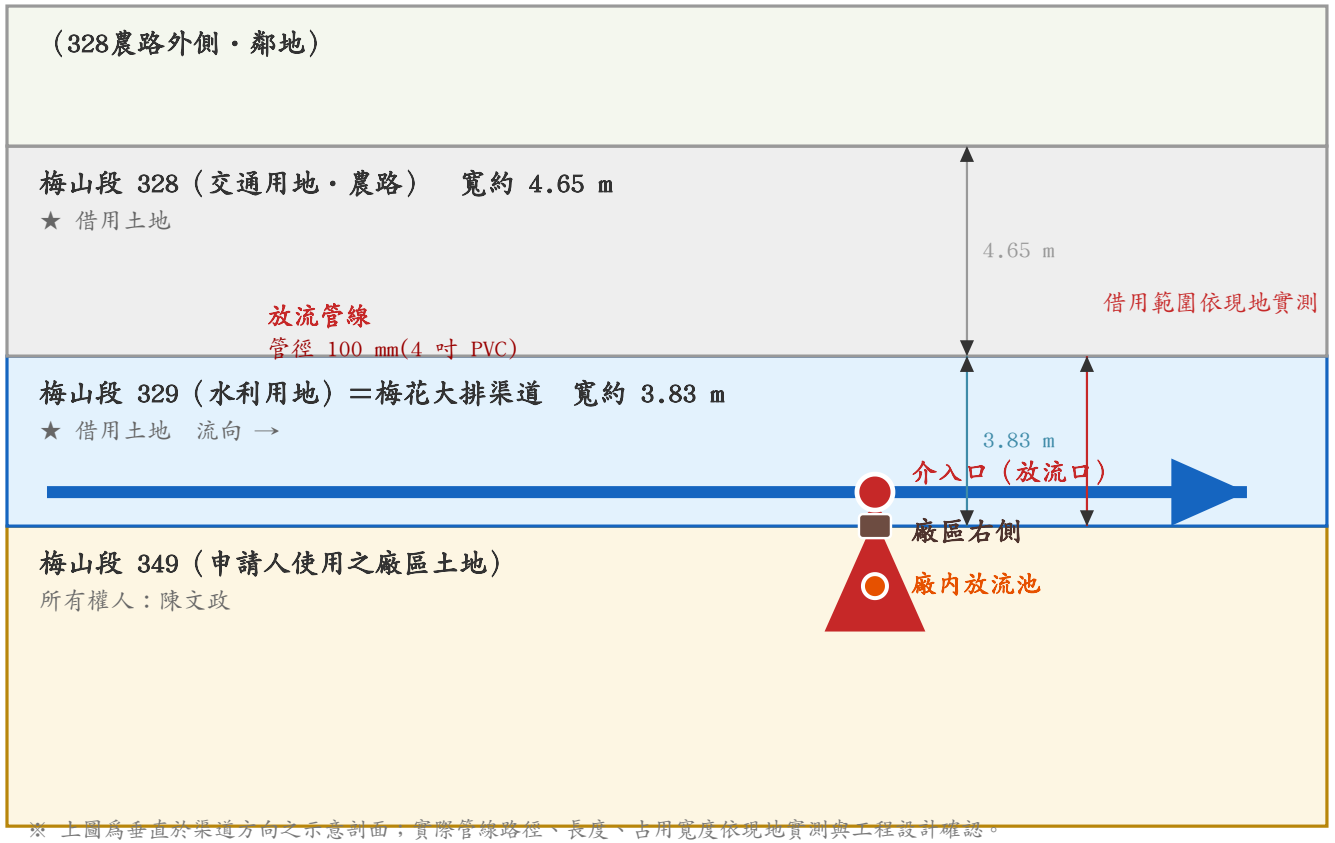


※ 上圖為垂直於渠道方向之示意剖面，實際管線路徑、長度、占用寬度依現地實測與工程設計確認。

## 鄰接公有土地明細

| 地號 | 用地類別 | 通過長度 | 面積 |
|---|---|---|---|
| 梅山段329 | 水利用地 | 約 3.83 m | 2,090.9㎡ |
| 梅山段328 | 交通用地 | — | 5,123.8㎡ |

占用寬度：以管徑計（約 0.1 m）
埋設深度：約 0.3～0.6 m(依現場)
施設方式：■ 埋管　□ 附掛　□ 明溝銜接
兩筆土地均為公有性質用地。依官方
應檢附文件三，需使用之土地如已依
農田水利法第23條第1項納入農田水利
事業作業基金者，得免附土地使用同意
證明；權屬請調謄本並洽羅東工作站確認。

## 施設承諾

1. 管線施設不妨礙農路通行及渠道通水。
2. 施工前 7 日通知管理處及羅東工作站，會同放樣後始得施工。
3. 路面及護岸開挖後即時復舊，回復原狀。
4. 損壞農田水利設施或農路者，由本公司負責無條件修復或賠償。
5. 許可期間屆滿或廢止時，自費拆除管線並回復原狀。

## 介入口坐標（TWD97）

E　325727.90
N　2726851.58
椿號：依初勘實測為準

**圖四　借用他人土地管線位置圖說**
管線通過梅山段329地號（梅花大排渠道）
案名：政達木業有限公司二廠生活污水搭排
示意圖（尺寸得實測）｜ TWD97 二度分帶 ｜ 第 4 張，

註：本圖為官方應檢附文件「借用他人土地者，應含設置於其土地管線位置圖說」之圖說。實際借用範圍、長度及是否須另取得土地使用同意，依地籍謄本權屬及管理處初勘結果為準。

# 圖五　排水系統流路圖

**員工廁所、盥洗、廚房**
生活污水產生源　作業人數 5 人

▼

**集污管線**
廠內埋設　PVC 管徑 100 mm

▼

**化糞池／污水處理設施**
既有化糞池　定期委託清運

▼

**放流池／人孔**
設置於廠區正門口側

▼

**累計流量計**
逐日記錄排放水量，備供稽查

▼

**介入口（放流口）**
梅山段 329 地號（水利用地）　型式：■埋管 □附掛 □明溝銜接

▼

**梅花排水**
名稱：梅花排水（梅花大排）　性質：排水渠道

## 排放水量

| | |
|---|---|
| 作業人數 | 5 人 |
| 單位污水量 | 150 公升／人·日 |
| 日平均排放量 | 0.75 m³ |
| 尖峰係數 | 3.0 |
| 日最大排放量 | 2.25 m³ |
| 年搭排日數 | 365 日 |
| 年最大排放量 | 821.25 m³ |

## 計算依據

內政部「建築物污水處理設施設計技術規範」
表2-1　C-1 工廠（廠房）類
單位污水量 150 公升／人·日
（規範得按作業人數1/4計，本案不折減，
以全員5人計算，屬保守估計）

## 排放水性質

僅生活污水（廁所、盥洗、廚房）
無製程廢水：木材裁切、刨光、砂磨、
組裝、乾燥等乾式加工，製程不產生廢水
納管申請書已聲明：屬低污染行業別，
製程不含脫脂、酸洗、電鍍或陽極處理
（納管編號 P0200190）


註：管線位置及高程依縣府、農田水利署會同放樣確認。

**圖五　排水系統流路圖**
生活污水自產生源至承受水體

案名：政達木業有限公司二廠生活污水搭排
示意圖（無比例）　|　TWD97 二度分帶　|　第 5 張，共 6


# 圖六　介入口工程設計圖（平面・剖面）

## （一）平面圖

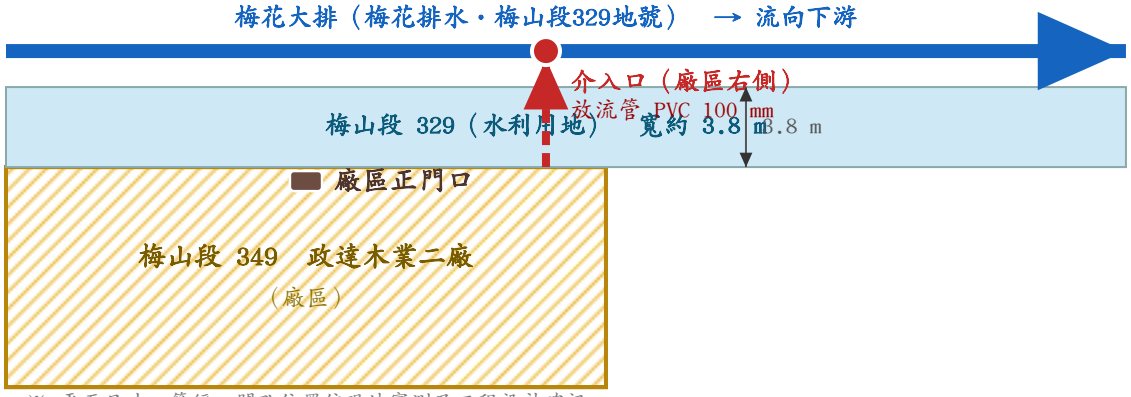


※ 平面尺寸、管徑、開孔位置依現地實測及工程設計確認

## （二）縱剖面圖

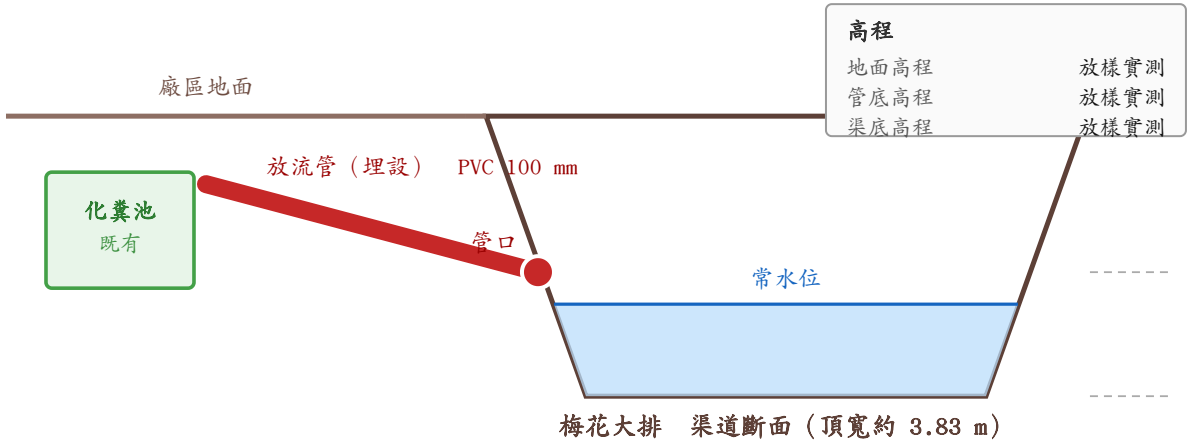


※ 高程、管徑、渠道斷面尺寸依現地實測填寫；施工前7日通知管理處及工作站會同放樣。

### 介入口規格

| | |
|---|---|
| 介入口型式 | ■ 埋管　□ 附掛　□ 明溝銜接 |
| 管材 | PVC |
| 管徑 | 100 mm(4 吋) |
| 管底高程 | 放樣實測 |
| 渠道底高程 | 放樣實測 |
| 渠道斷面（寬×深） | 頂寬約 3.83 m |
| 護岸開孔尺寸 | 約 φ15 cm |
| 回填與復舊方式 | 砂回填、原狀復舊 |
| 施工廠商 | 核准後選定報府 |

### 施工承諾事項

1. 施工前 7 日通知管理處及羅東工作站，會同放樣後始得施工。
2. 施工期間不阻斷渠道通水，必要時設置臨時導水設施。
3. 施工損壞農田水利設施者，由本公司負責無條件修復或賠償。
4. 竣工後 30 日內報請管理處查驗。
5. 避開灌溉期施工；如須於灌溉期施工，事先報經管理處同意。
6. 工程費用由本公司負擔。

**圖六　介入口工程設計圖**

平面圖・縱剖面圖

案名：政達木業有限公司二廠生活污水搭排示意圖（尺寸待實測）　|　TWD97 二度分帶　|　第 6 張，